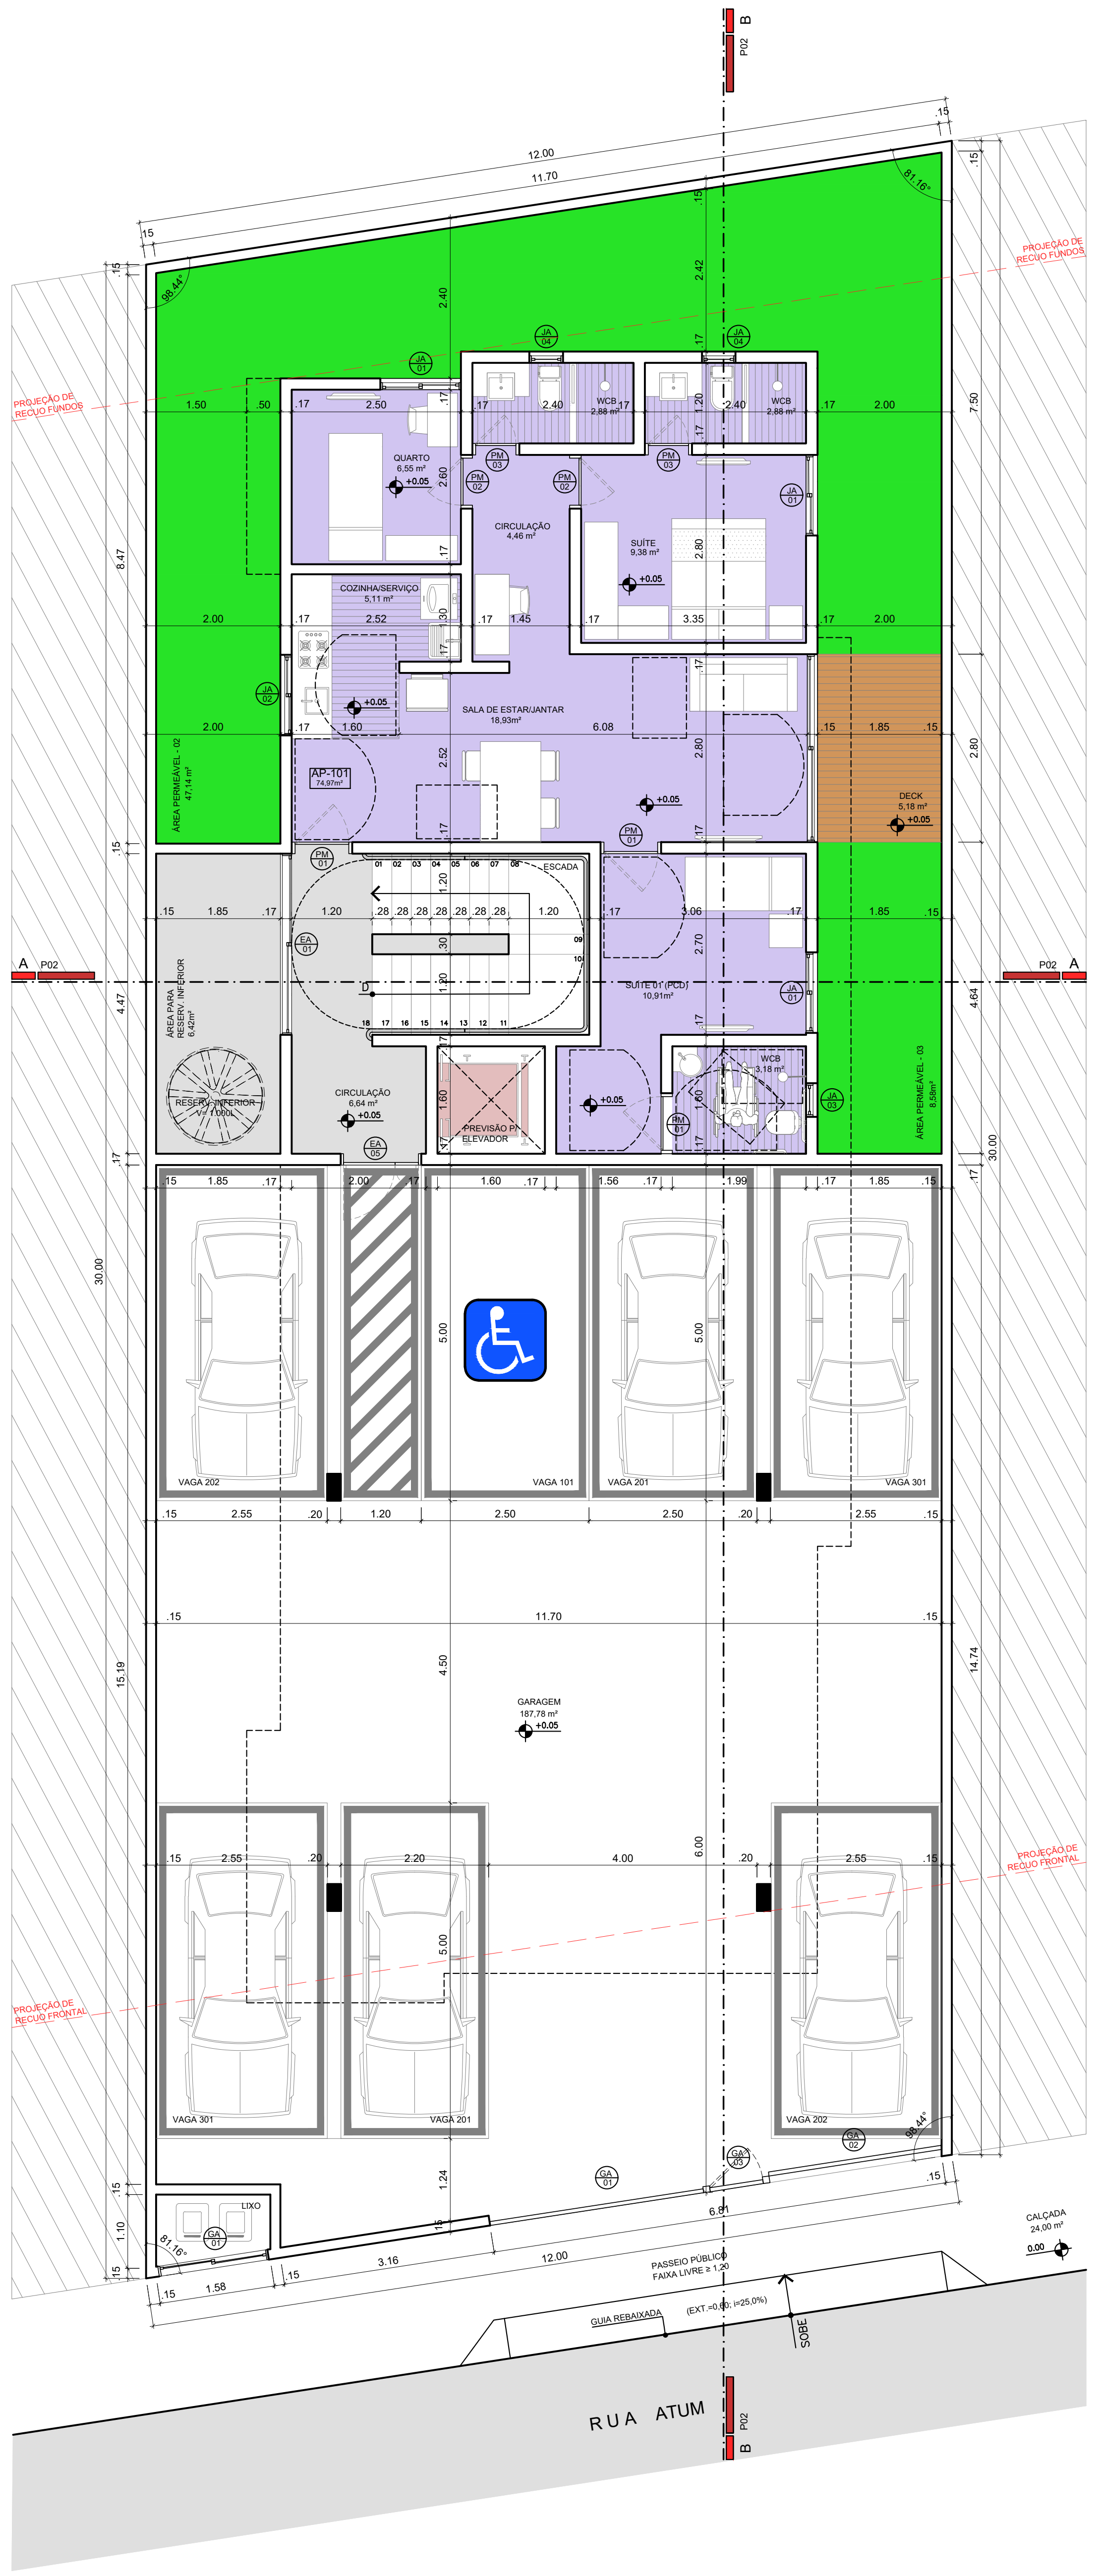

02 PLANTA BAIXA PAV. TÉRREO
P01 RESIDÊNCIA MULTIFAMILIAR ESC. 1/75
NM

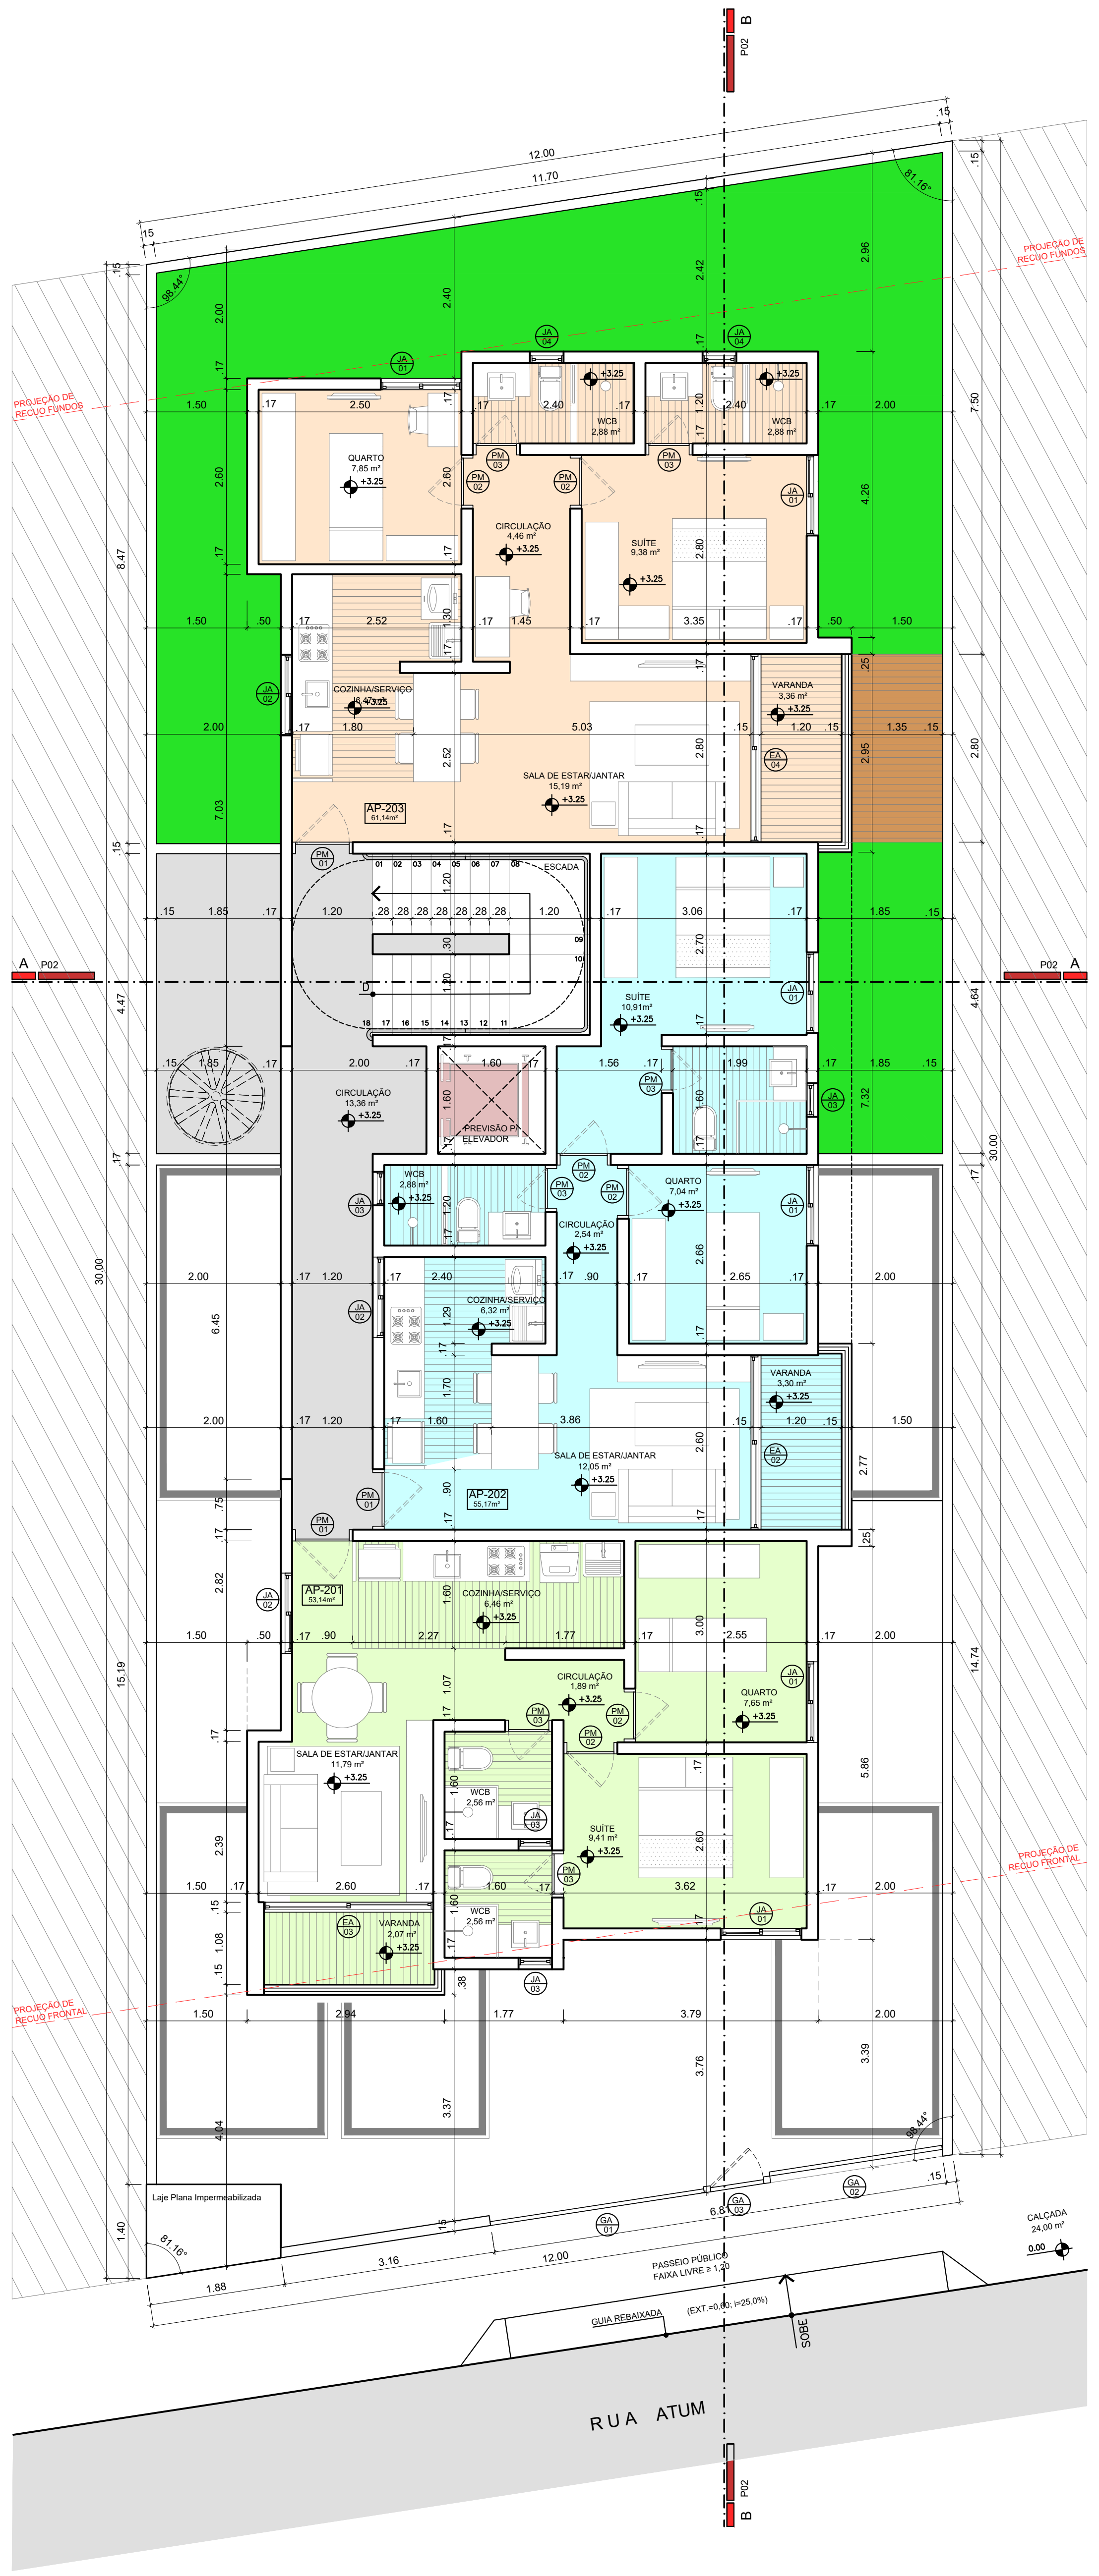

03 PLANTA BAIXA 1º PAVIMENTO
P01 RESIDÊNCIA MULTIFAMILIAR ESC. 1/75
NM

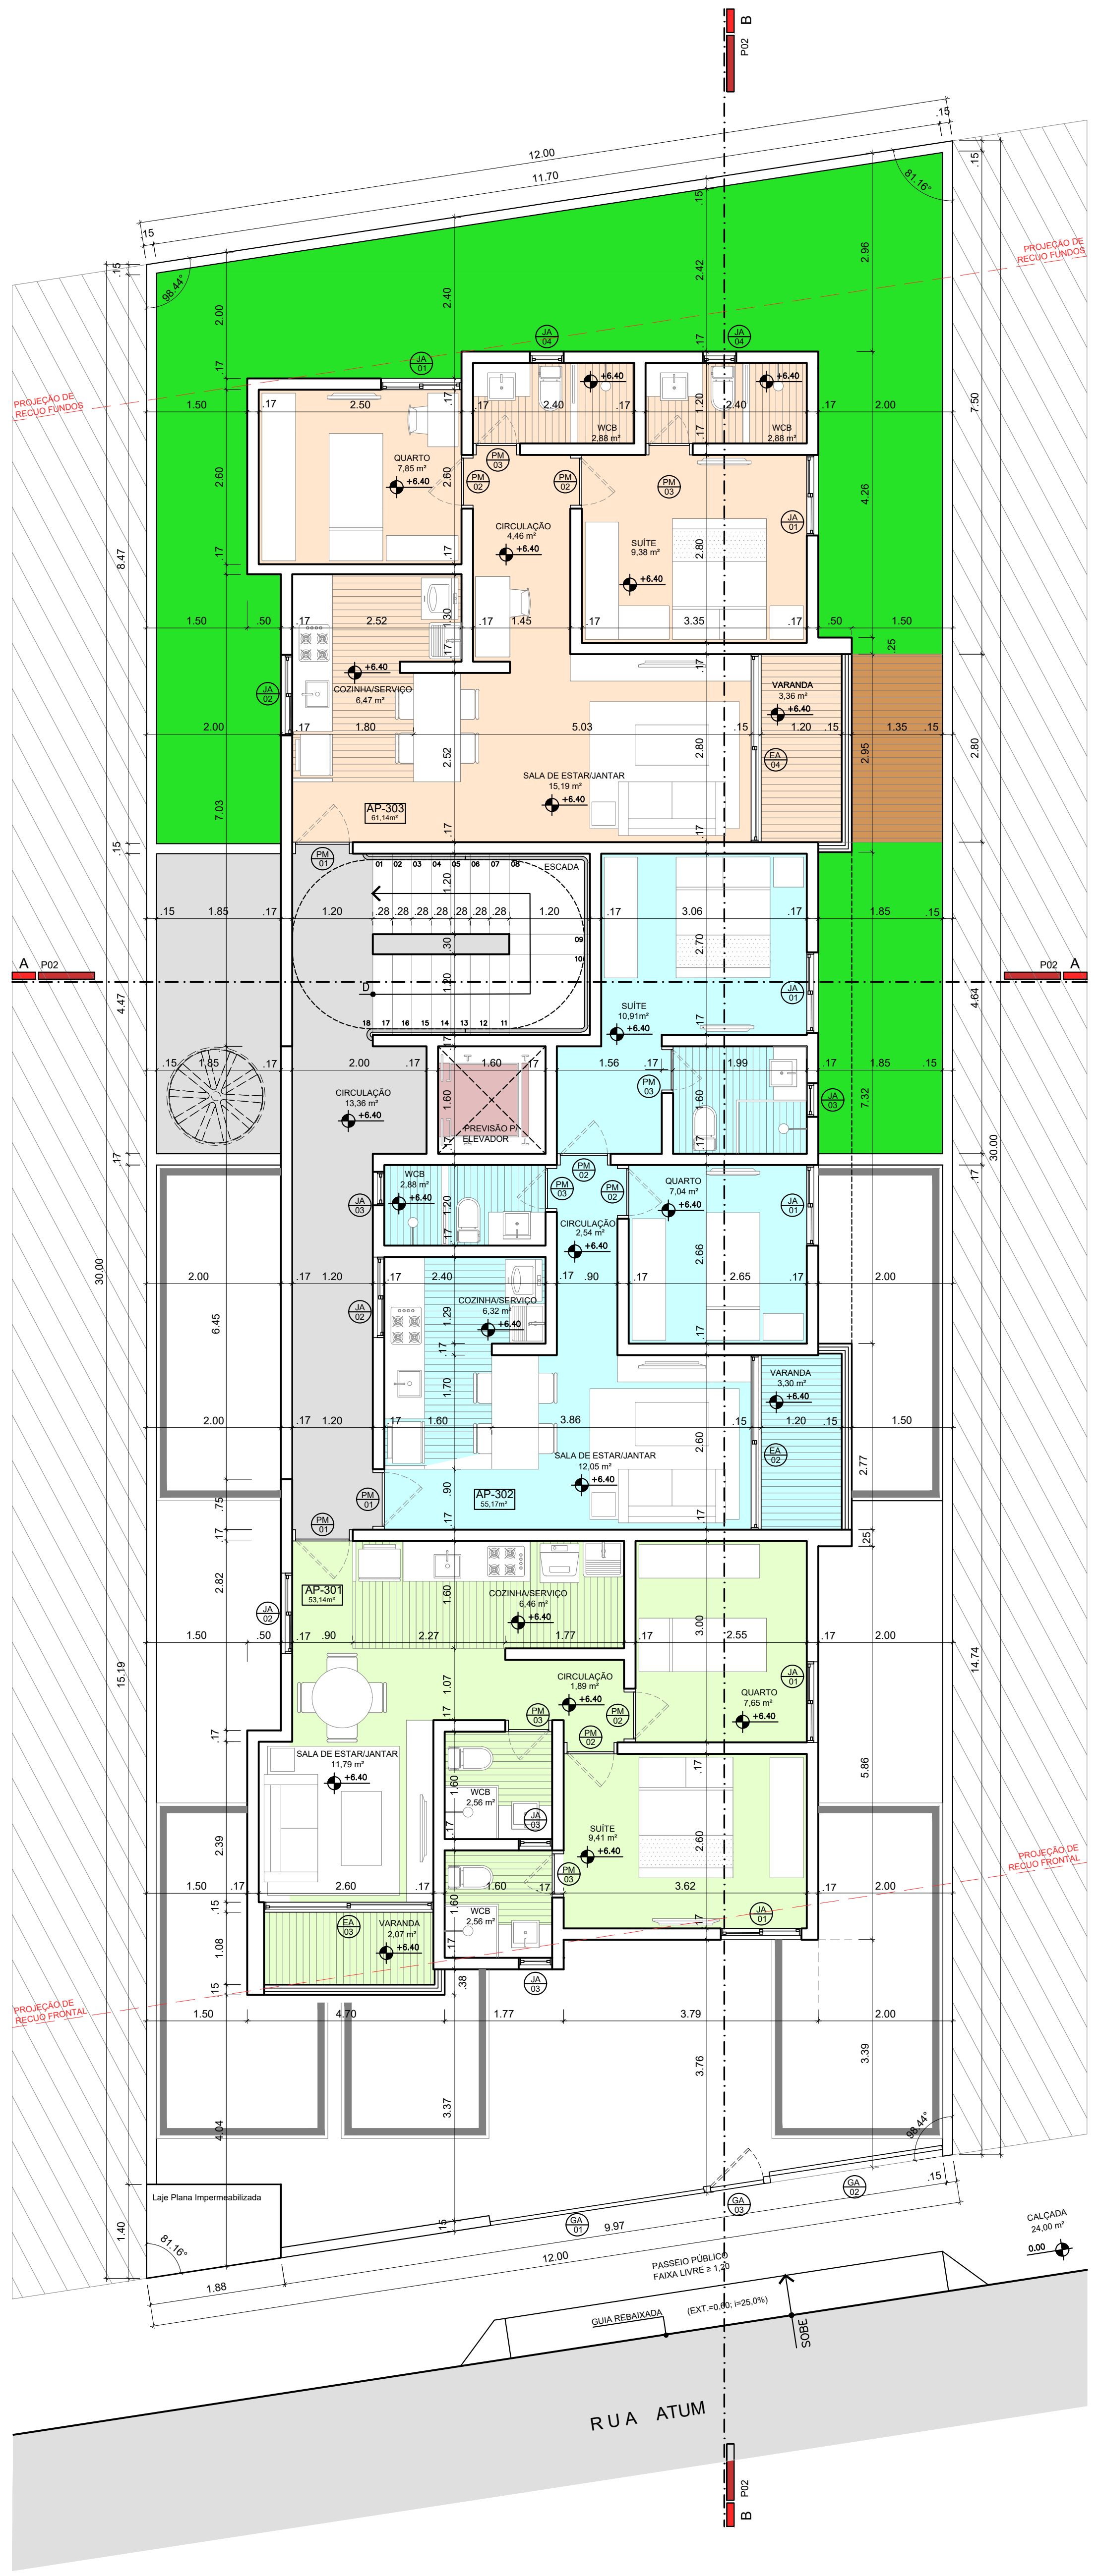

04 PLANTA BAIXA 2º PAVIMENTO
P01 RESIDÊNCIA MULTIFAMILIAR ESC. 1/75
NM

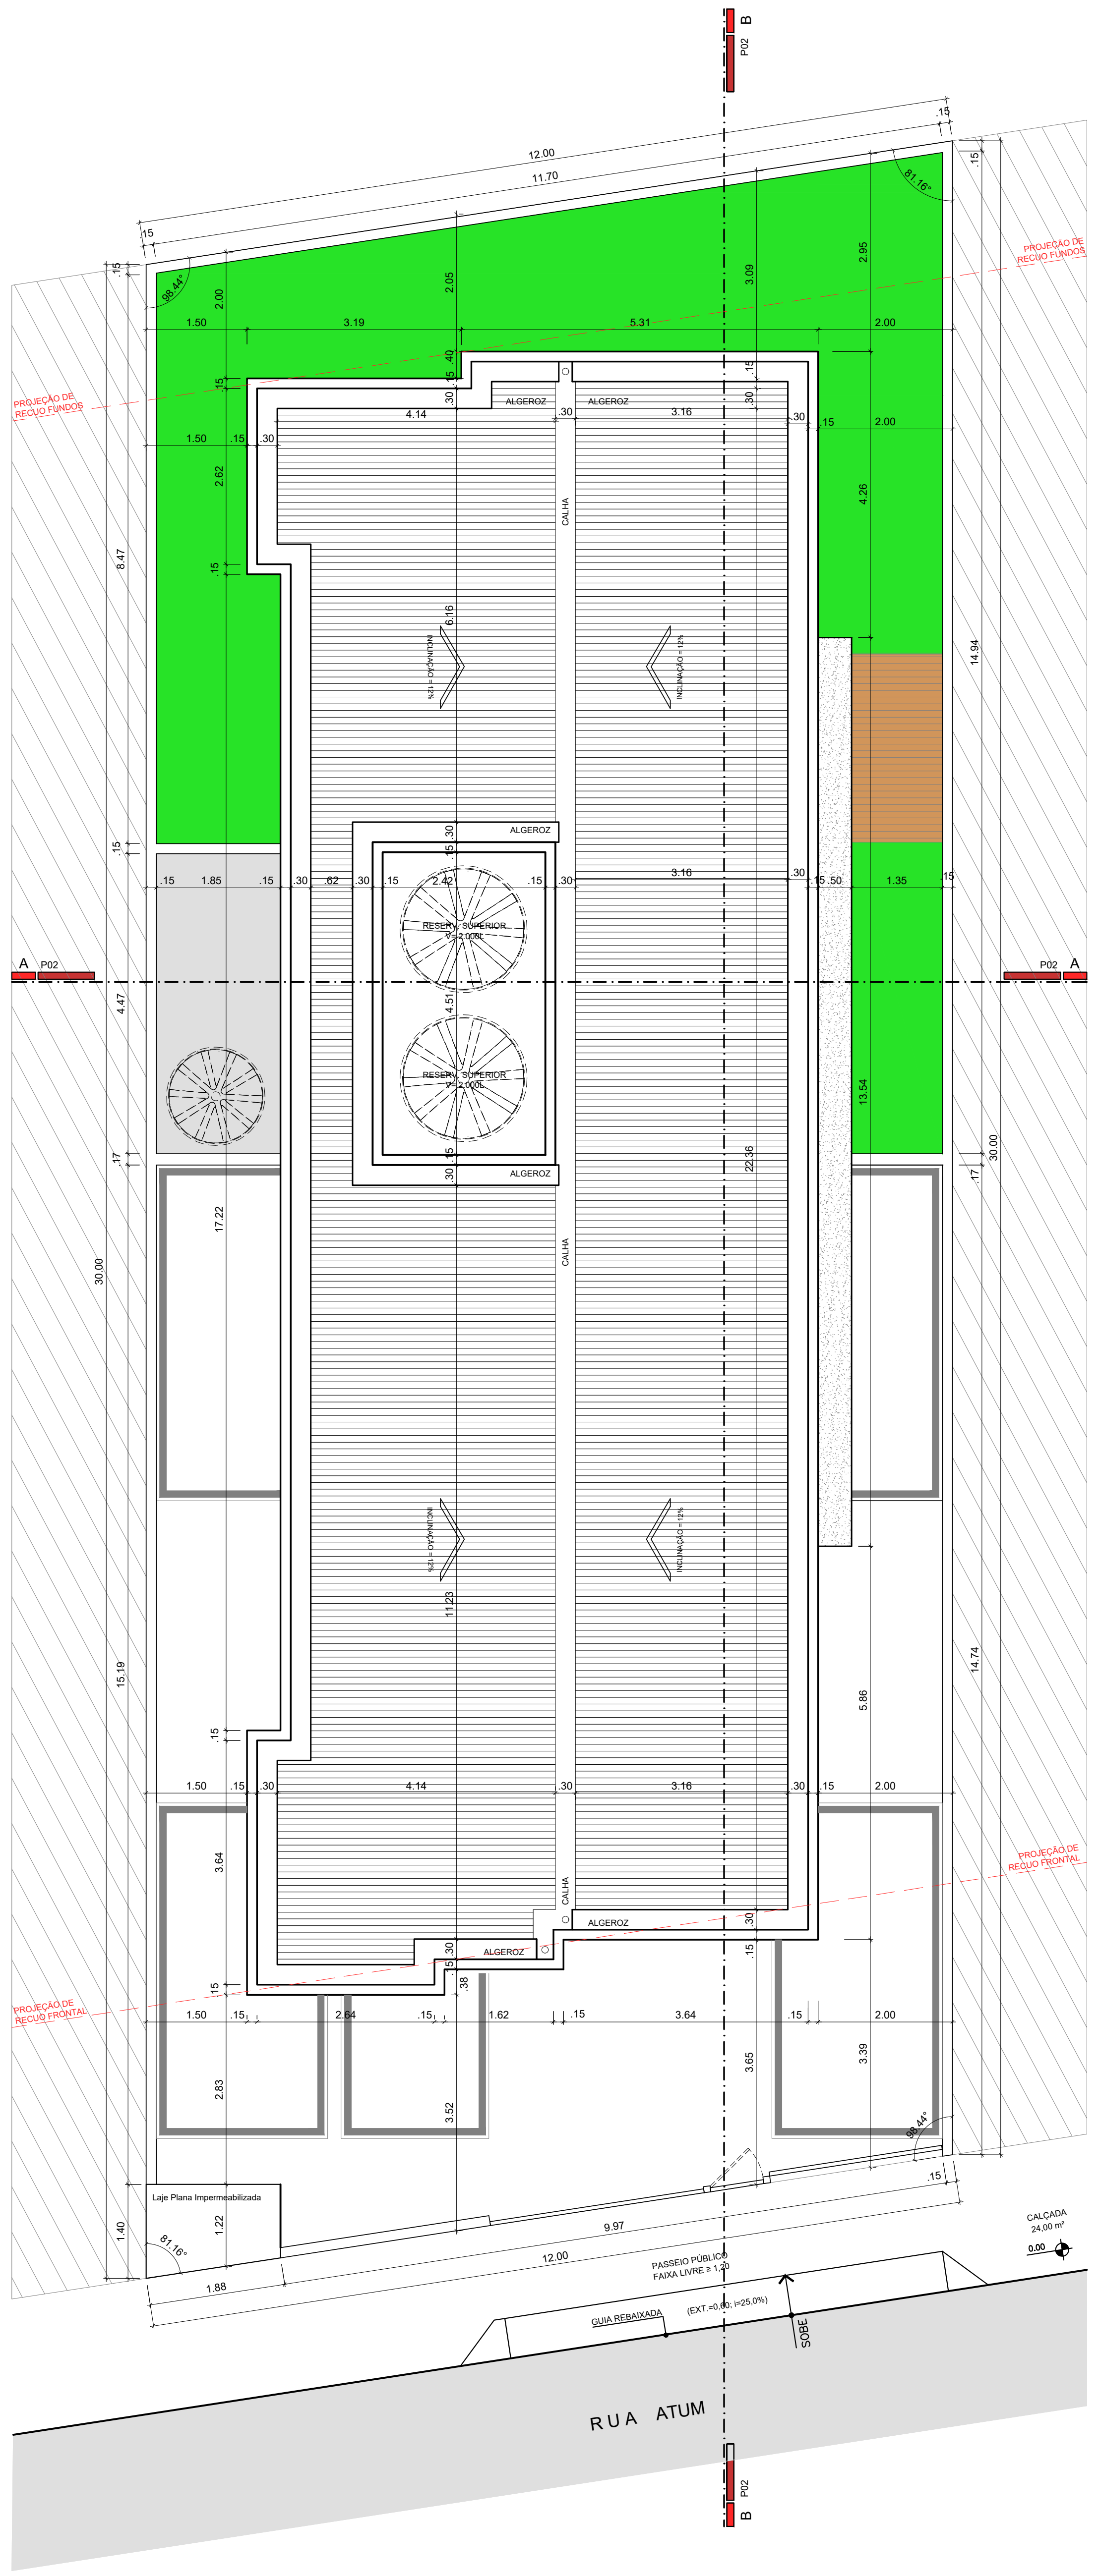

05 PLANTA DE LOCAÇÃO E COBERTA
P01 RESIDÊNCIA MULTIFAMILIAR ESC. 1/75
NM

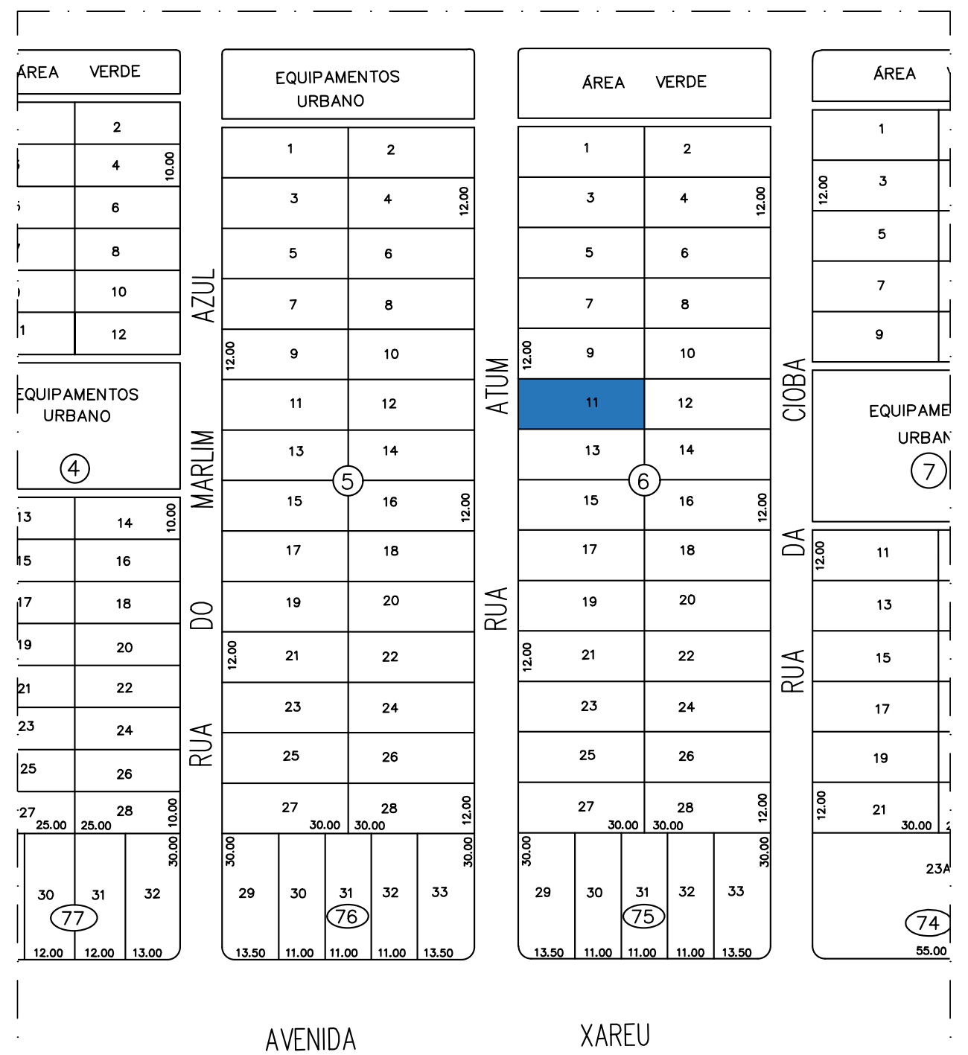

1 PLANTA DE LOCALIZAÇÃO
P01 RESIDÊNCIA MULTIFAMILIAR ESC. 1/1800

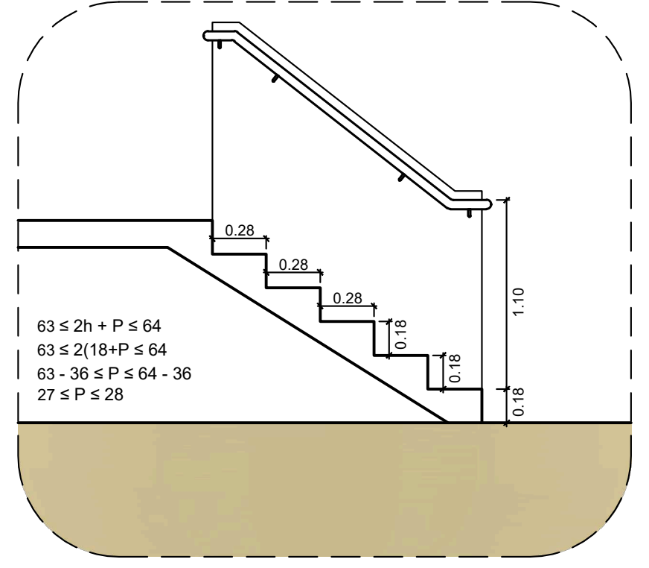

$63 \leq 2h + P \leq 64$
$63 \leq 2(18+P \leq 64$
$63 - 36 \leq P \leq 64 - 36$
$27 \leq P \leq 28$

12 DET. DA ESCADA
P02 RESIDÊNCIA MULTIFAMILIAR ESC. 1/25

QUADRO DE ESQUADRIAS

ESQUADRIAS	LOCAL	DIMENSÃO (L x H)	QUANTIDADE	MATERIAL
EA01	CIRCULAÇÃO TÉRREO	2.70 x 2.10	01	ALUMÍNIO
EA02	SALAS DE ESTAR	2.60 x 2.10	05	ALUMÍNIO
EA03	SALAS DE ESTAR	2.50 x 2.10	02	ALUMÍNIO
EA04	ACESSO SOCIAL	1.20 x 2.10	01	ALUMÍNIO

ESQUADRIAS	LOCAL	DIMENSÃO (L x H)	QUANTIDADE	MATERIAL
JA01	QUARTOS/SUÍTES	1.20 x 1.10	15	ALUMÍNIO
JA02	COZINHA	1.20 x 0.50	07	ALUMÍNIO
JA03	WCS	0.50 x 1.00	09	ALUMÍNIO
JA04	WCS	0.50 x 0.50	06	ALUMÍNIO
PM01	ACESSO APTO./AP PCD	0.90 x 2.10	09	MADEIRA
PM02	QUARTOS	0.80 x 2.10	14	MADEIRA
PM03	WCS	0.70 x 2.10	14	MADEIRA
GA01	ACESSO AUTO PRINCIPAL	3.20 x 2.00	01	ALUMÍNIO
GA02	ACESSO AUTO INDIVIDUAL	2.60 x 2.00	01	ALUMÍNIO
GA03	ACESSO AUTO INDIVIDUAL	1.00 x 2.00	01	ALUMÍNIO
GA04	ACESSO LIXOS	1.50 x 2.00	01	ALUMÍNIO

OBS.: TODAS AS MEDIDAS DEVERÃO SER CONFERIDAS NA OBRA

Wellington A. de Oliveira
Arquiteto e Urbanista
CAU Nº A 51775-5

PROPRIETÁRIO ACTIVA CONSTRUÇÕES LTDA - CNPJ: 50.056.430/0001-01
PROJETO ARQ. WELLINGTON A. DE OLIVEIRA CAU Nº. A51775-5
CONSTRUÇÃO

PROJETO: CONSTRUÇÃO DE UMA EDIFICAÇÃO RESIDENCIAL MULTIFAMILIAR
LOCAL: LT-011, QD-06, DO LOTEAMENTO PORTAL DO POÇO - CABEDELO/PB
PROPRIETÁRIO: ACTIVA CONSTRUÇÕES LTDA

	ESCALA
PLANTA BAIXA PAV. TÉRREO	1/75
PLANTA BAIXA 1° PAVIMENTO	1/75
PLANTA BAIXA 2° PAVIMENTO	1/75
PLANTA DE LOCAÇÃO E COBERTA	1/75
	1/75
	1/75

E-MAIL
DATA MAIO/2026

01 / 02
PRANCHA

ÁREA DO TERRENO:....................................360,00m²
ÁREA TOTAL CONSTRUÍDA:.........................589,23m²
ÁREA PROJ. ORTOGONAL:...........................196,39m²
TAXA DE OCUPAÇÃO:...................................54,55%
INDICE DE APROVEITAMENTO:.........................1,636
ÁREA DE SOLO PERMEÁVEL:...........51,81m² =14,39%
VOLUME DA CAIXA D'ÁGUA:....................5000LITROS
ÁREAS:

ENNOVE
ARQUITETURA | ENGENHARIA
ennoveprojetos@gmail.com

PREFEITURA MUNICIPAL DE CABEDELO
Secretaria do Controle do Uso e Ocupação do Solo
VISTO
ASSINADO DIGITALMENTE
Setor de Análise

PREFEITURA MUNICIPAL DE CABEDELO
Secretaria do Controle do Uso e Ocupação do Solo
APROVADO
Processo nº 382/2026
Alvará nº 2026/000147.8
ASSINADO DIGITALMENTE
Secretário

Assinado por 2 pessoas: THIAGO PAES FONSECA DANTAS e ISABELLE DOS SANTOS FIGUEIREDO
Para verificar a validade das assinaturas, acesse https://cabedelo.1doc.com.br/verificacao/8F45-F04D-7449-9EB1 e informe o código 8F45-F04D-7449-9EB1

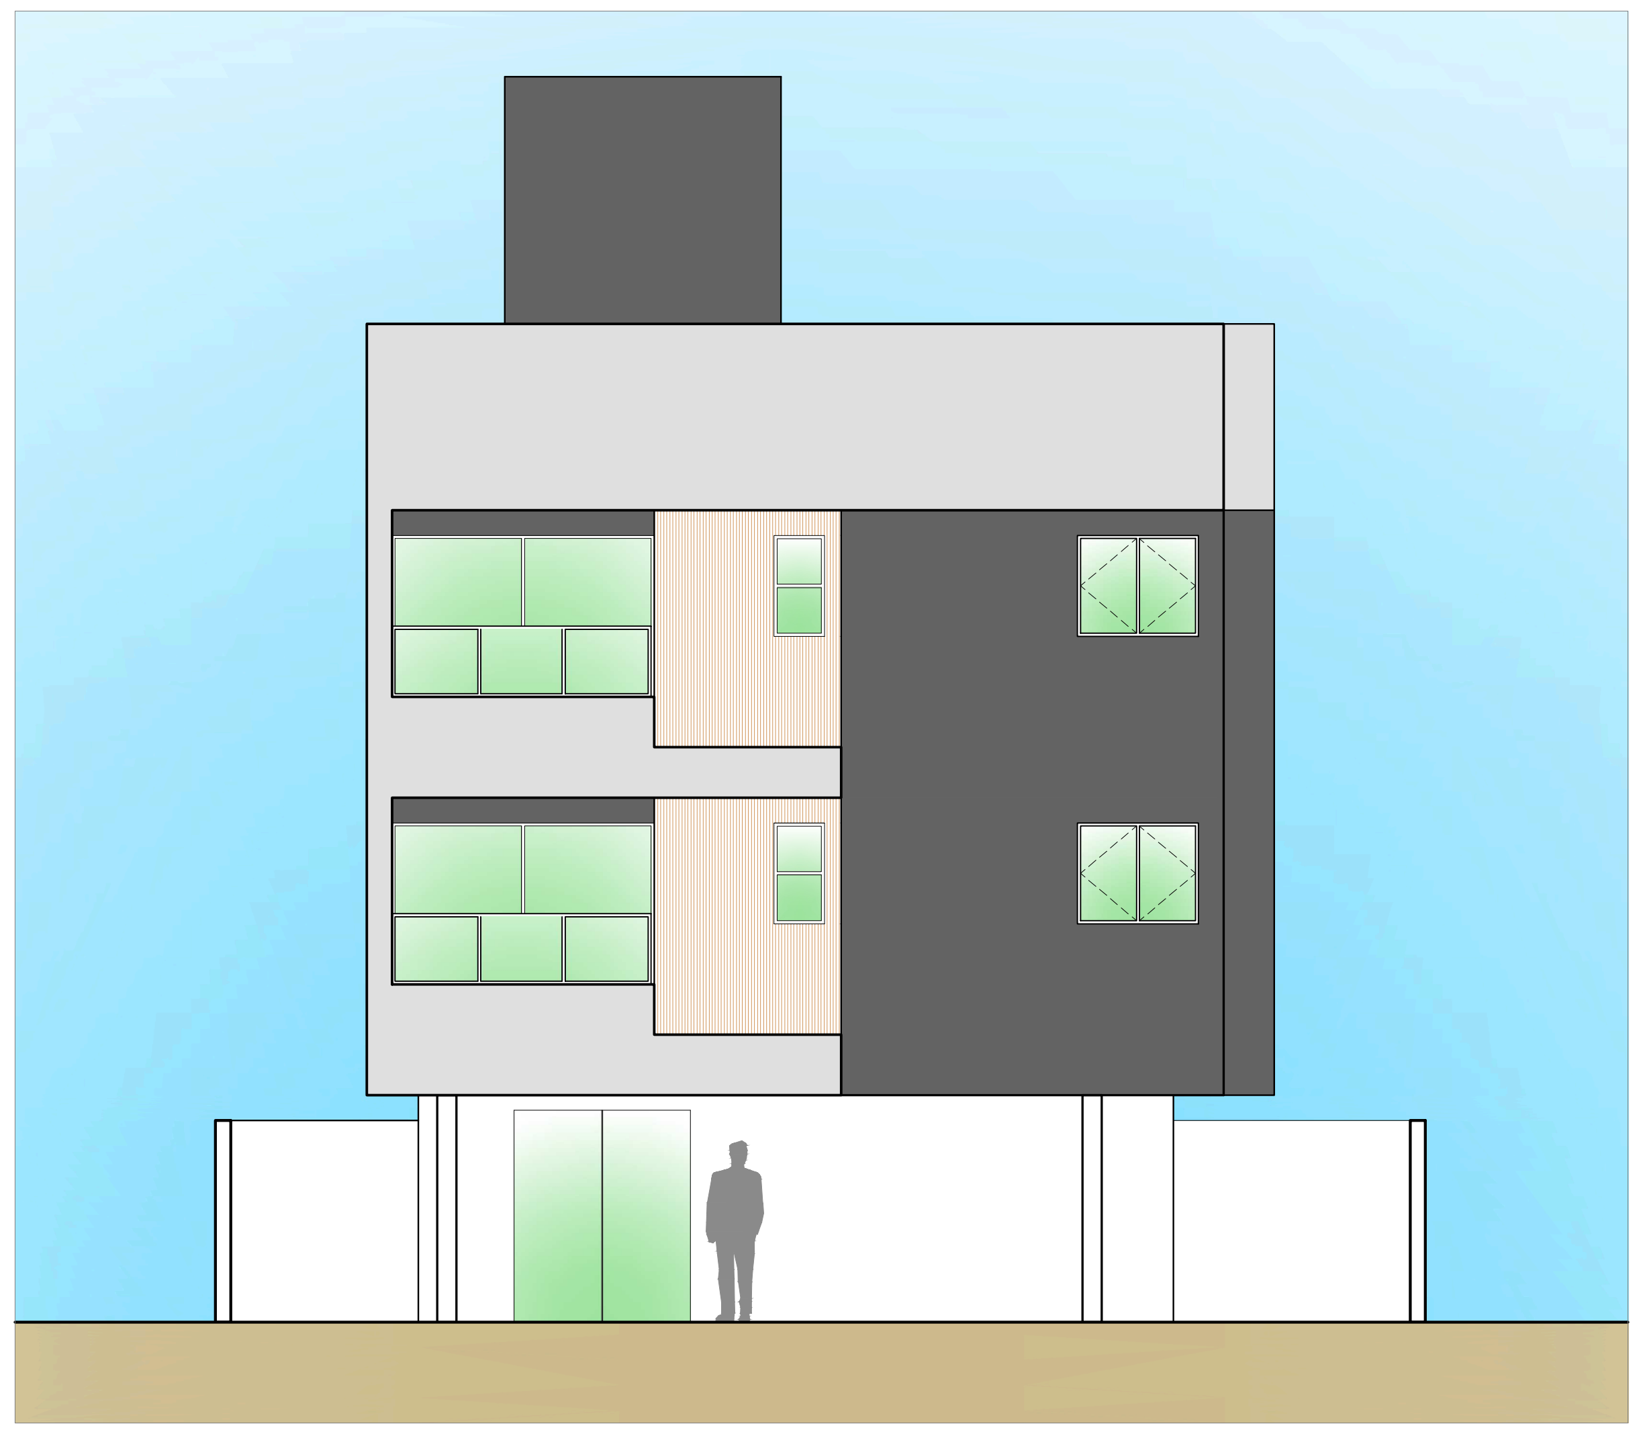

06 FACHADA SUL
P02 RESIDÊNCIA MULTIFAMILIAR ESC. 1/75

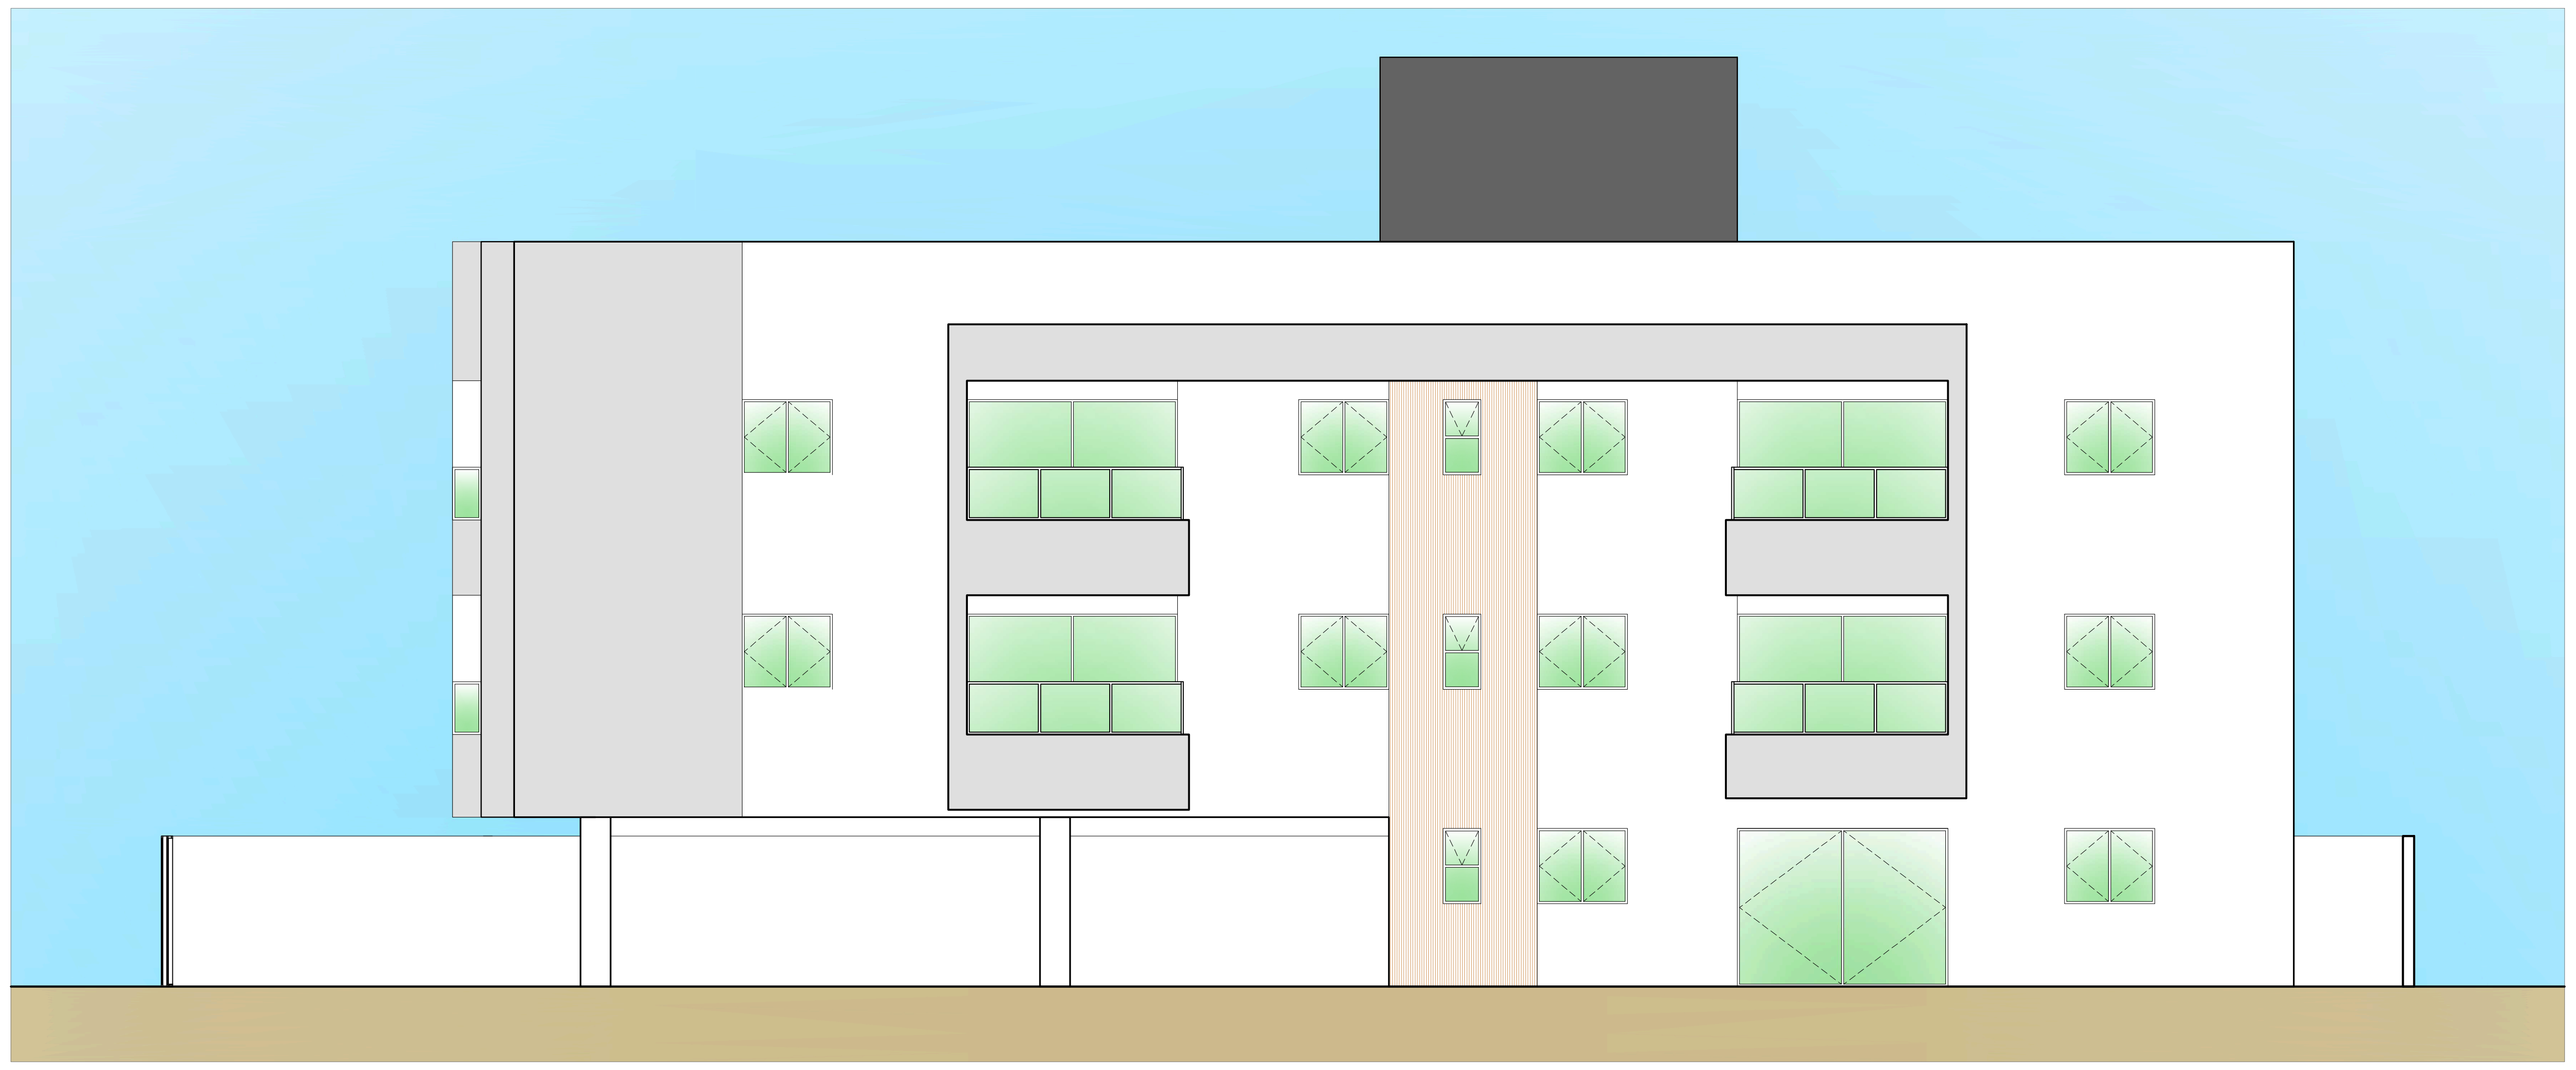

07 FACHADA LESTE
P02 RESIDÊNCIA MULTIFAMILIAR ESC. 1/75

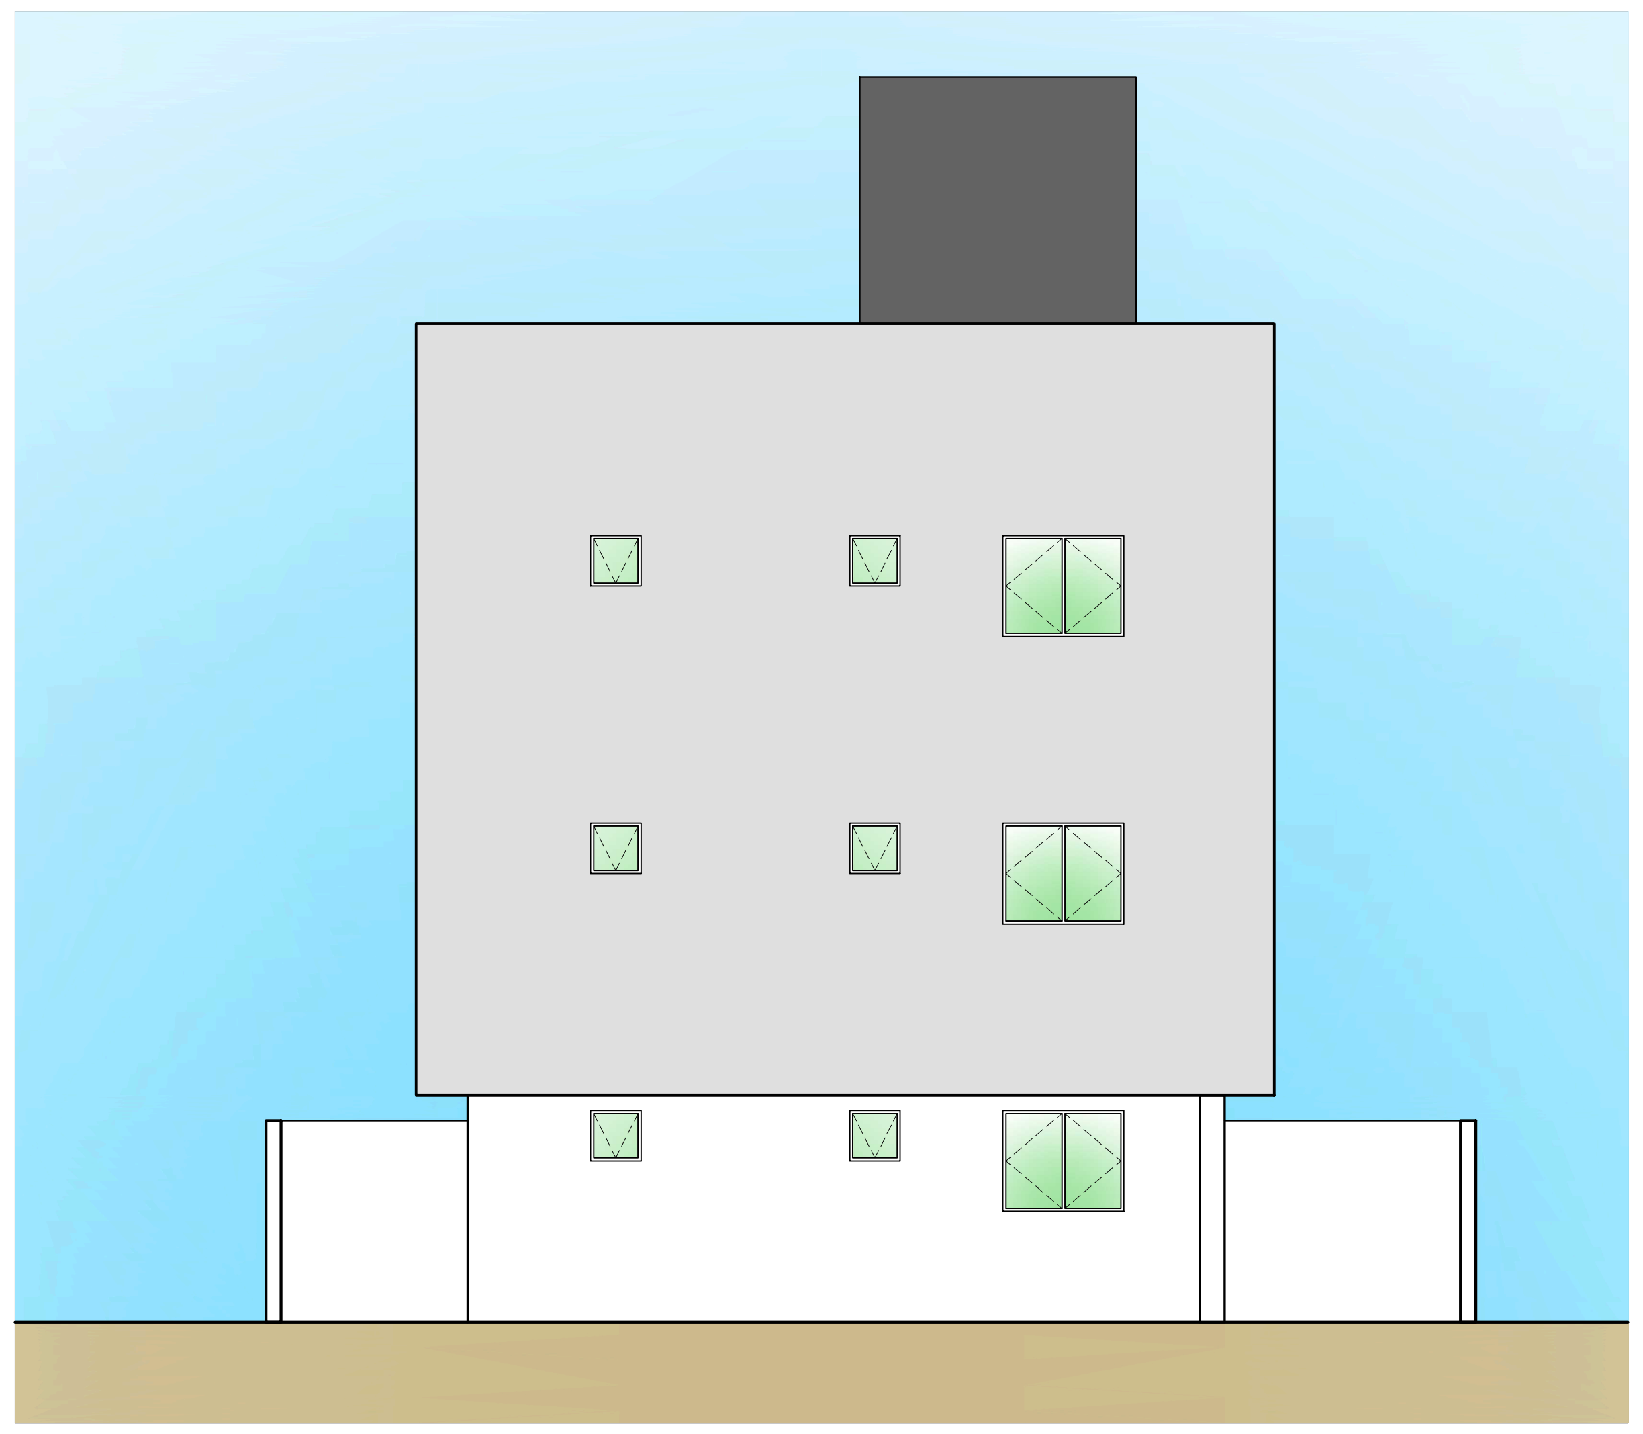

08 FACHADA NORTE
P02 RESIDÊNCIA MULTIFAMILIAR ESC. 1/75

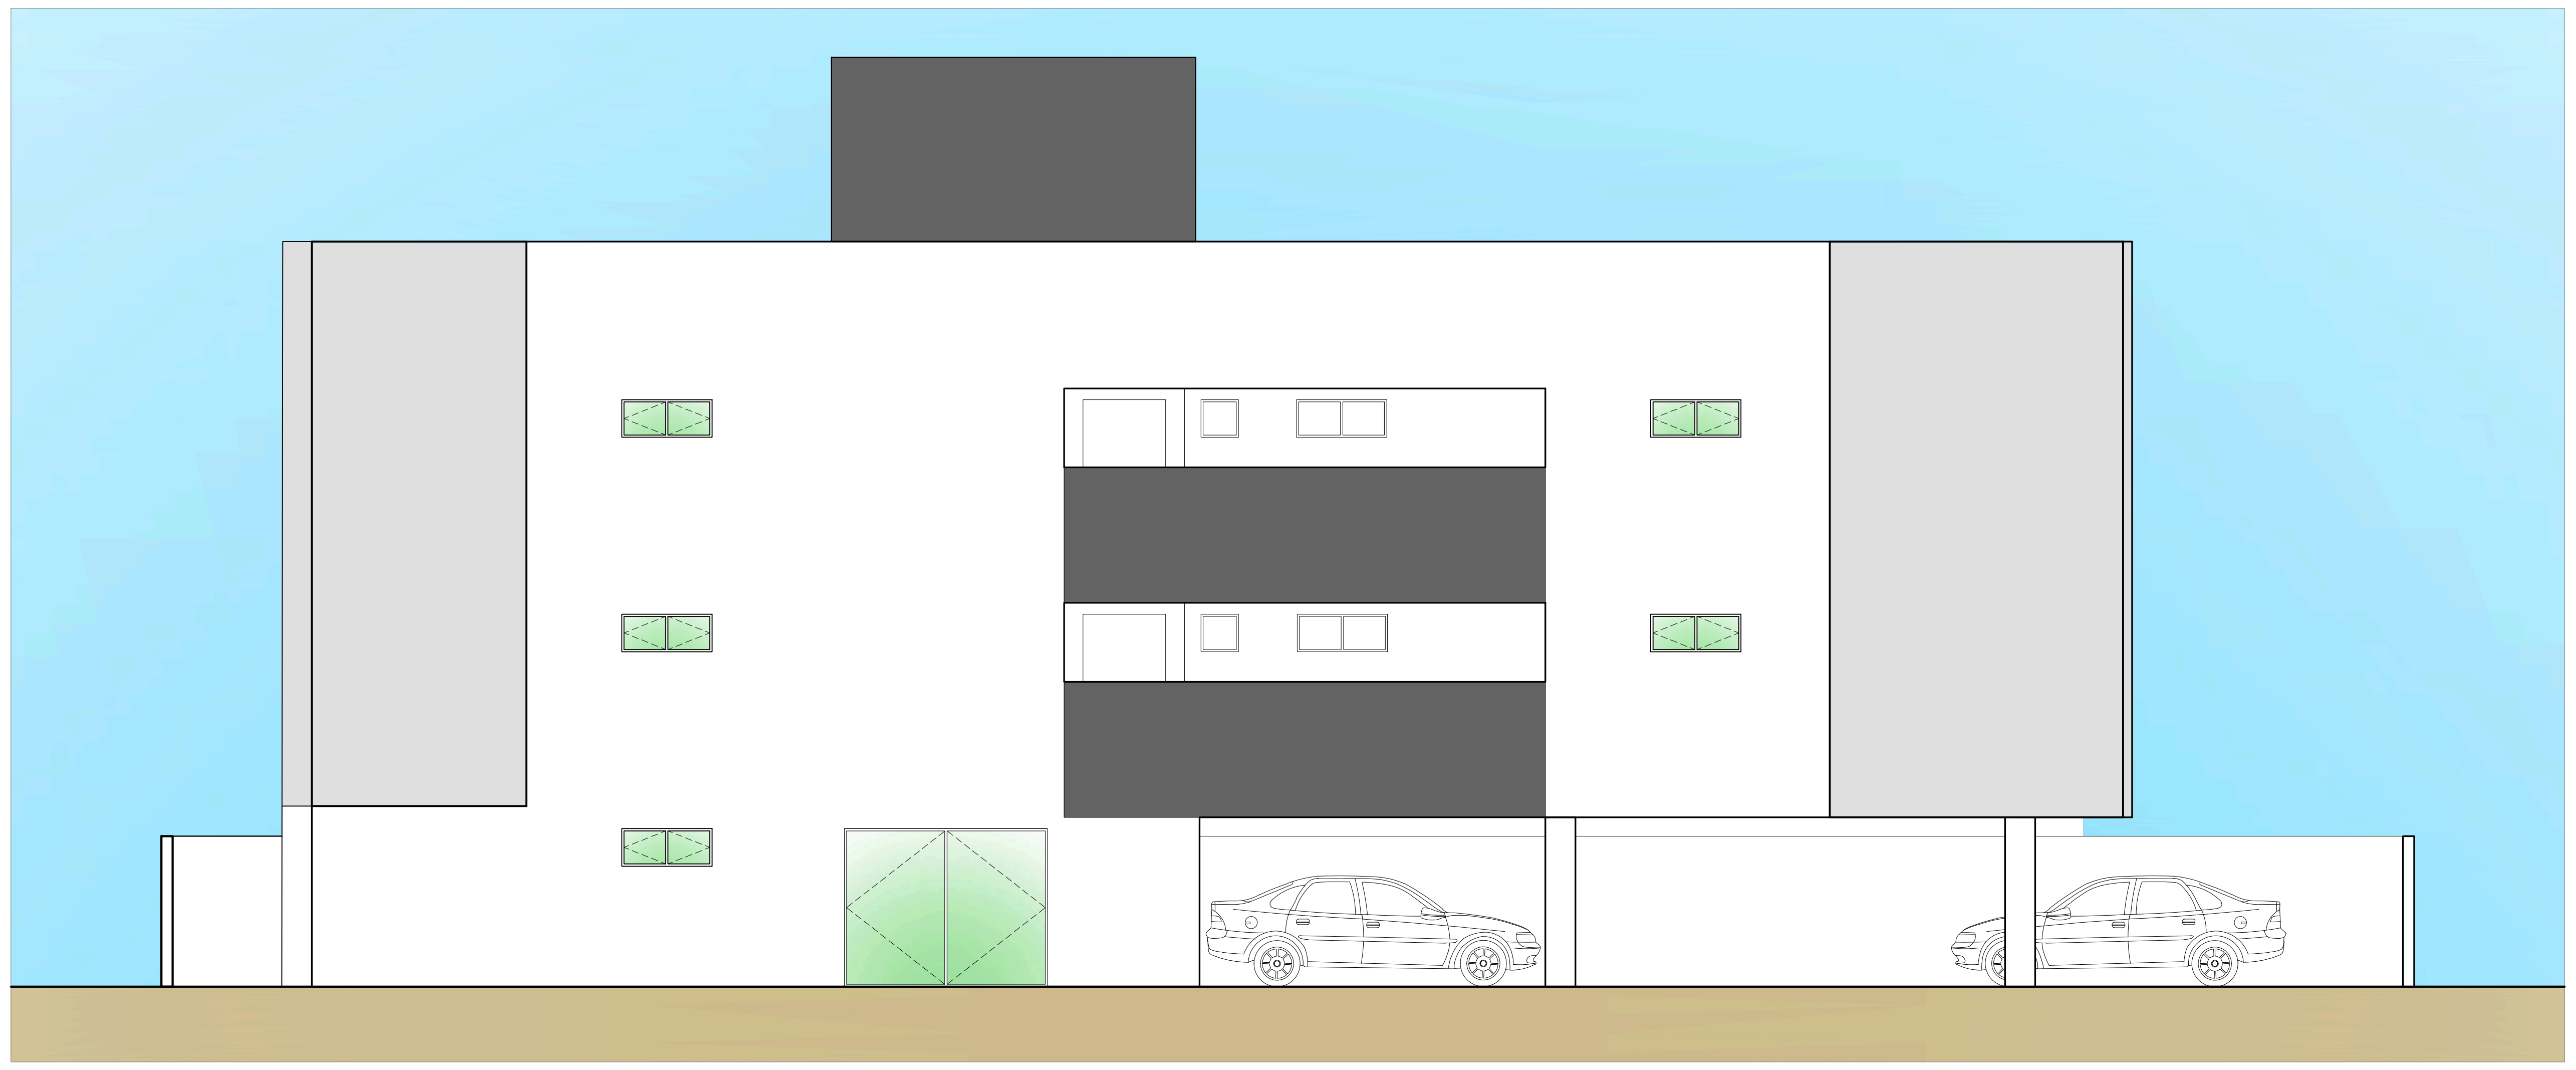

09 FACHADA OESTE
P02 RESIDÊNCIA MULTIFAMILIAR ESC. 1/75

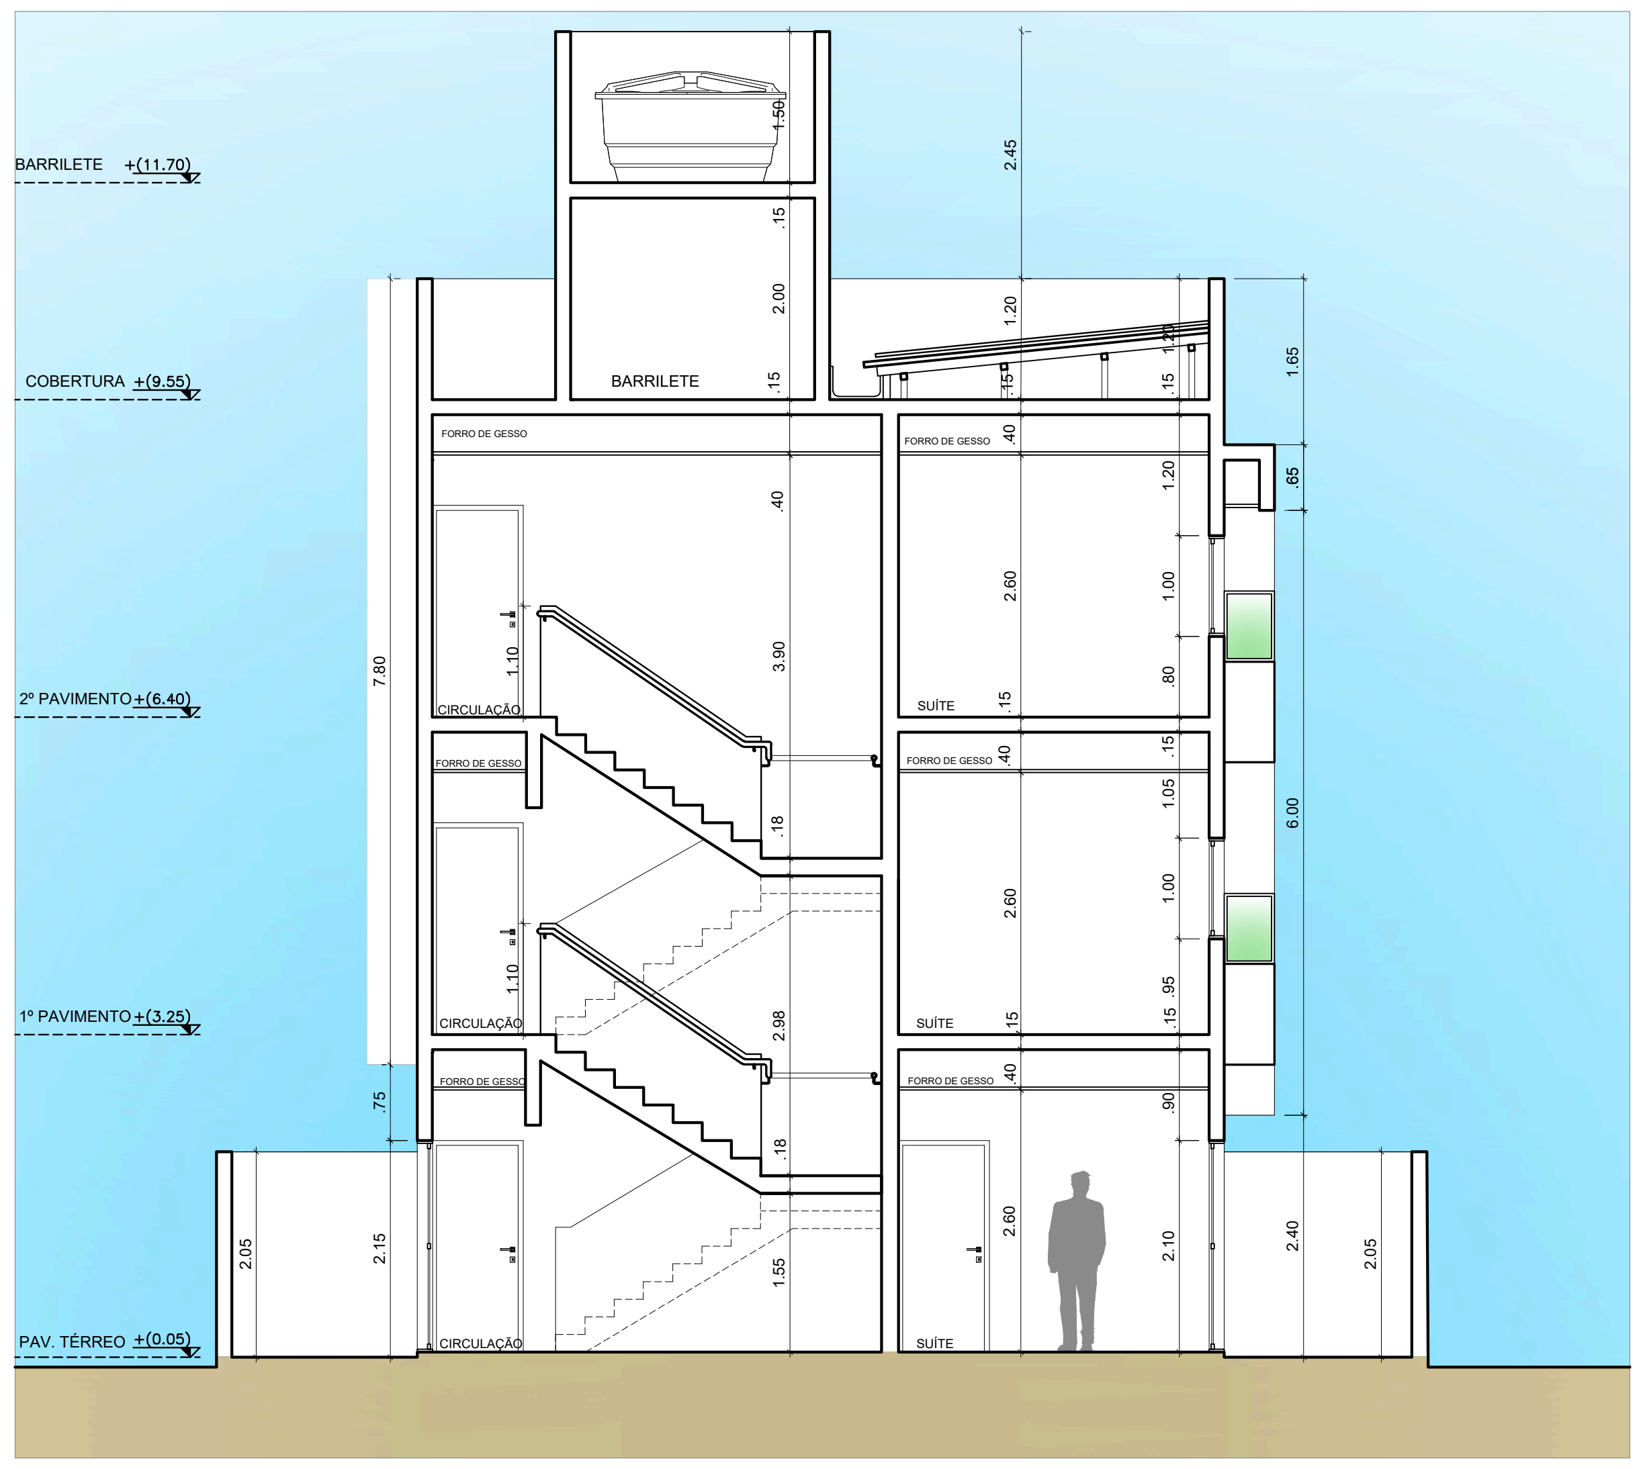

10 CORTE - AA
P02 RESIDÊNCIA MULTIFAMILIAR ESC. 1/75

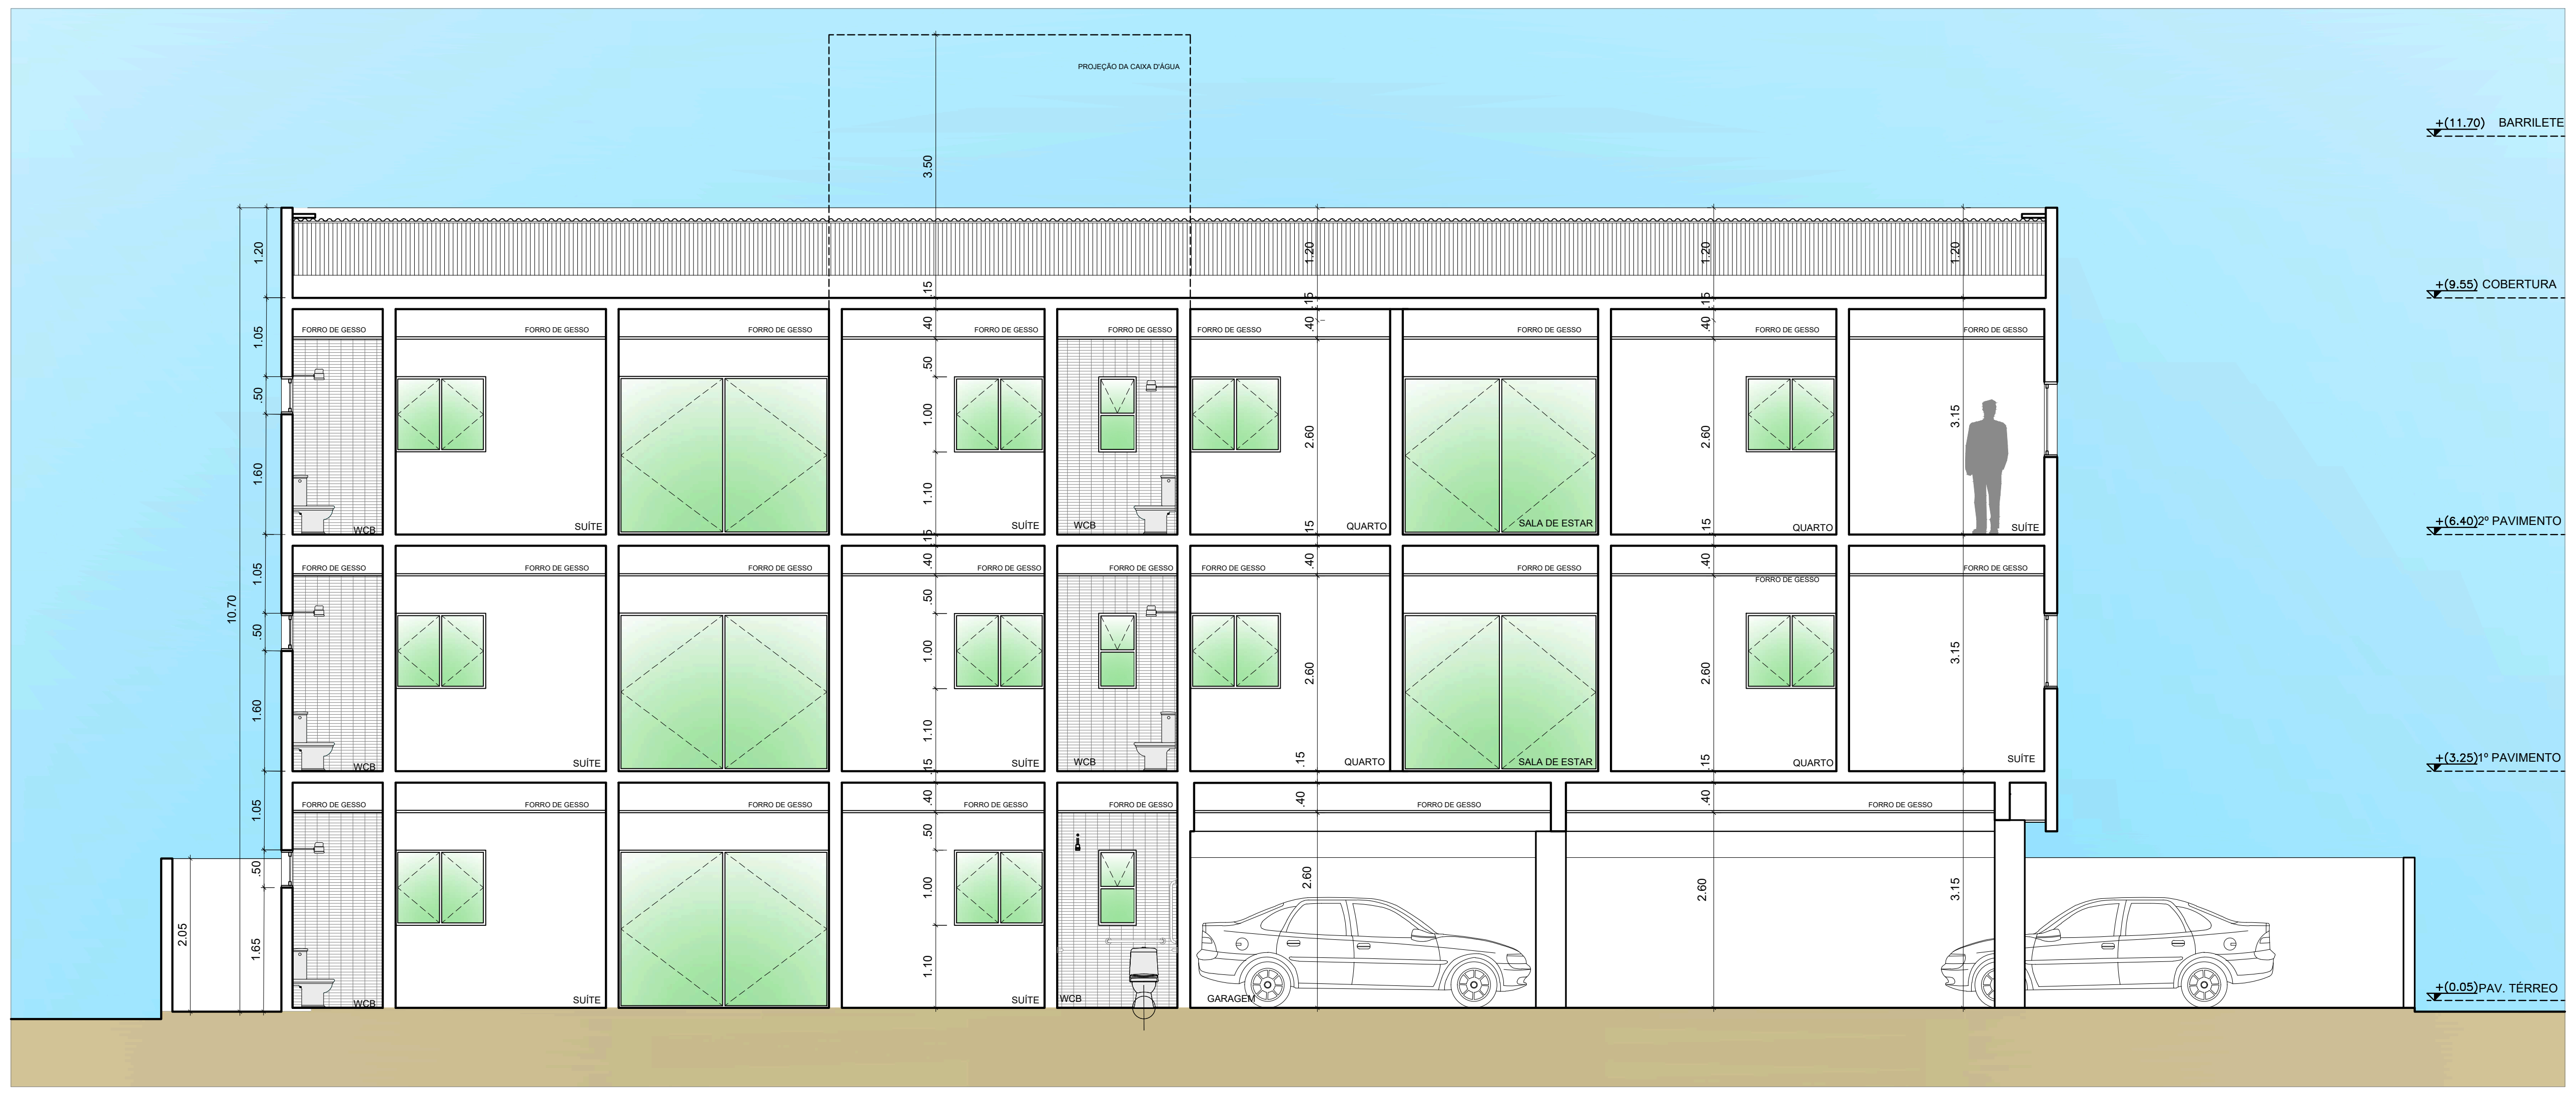

11 CORTE - BB
P02 RESIDÊNCIA MULTIFAMILIAR ESC. 1/75

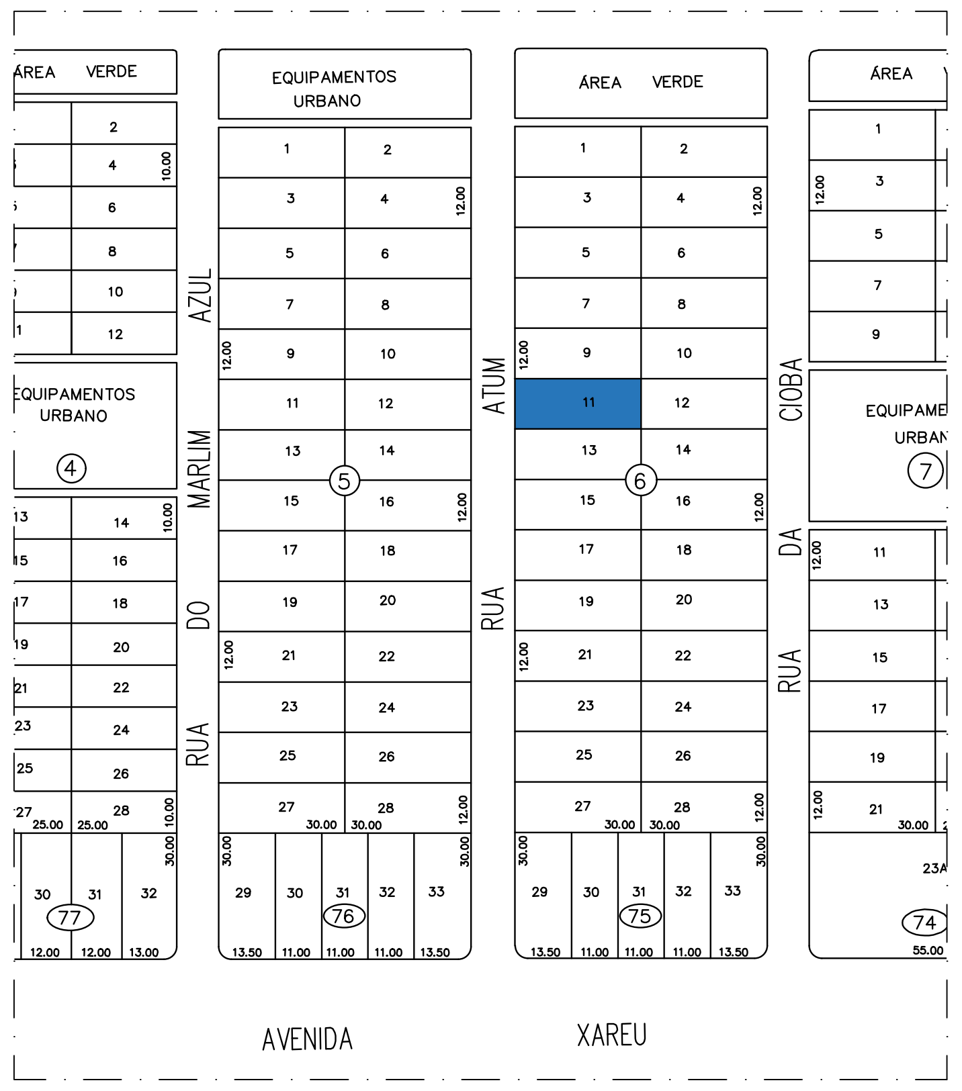

1 PLANTA DE LOCALIZAÇÃO
P01 RESIDÊNCIA MULTIFAMILIAR ESC. 1/1800

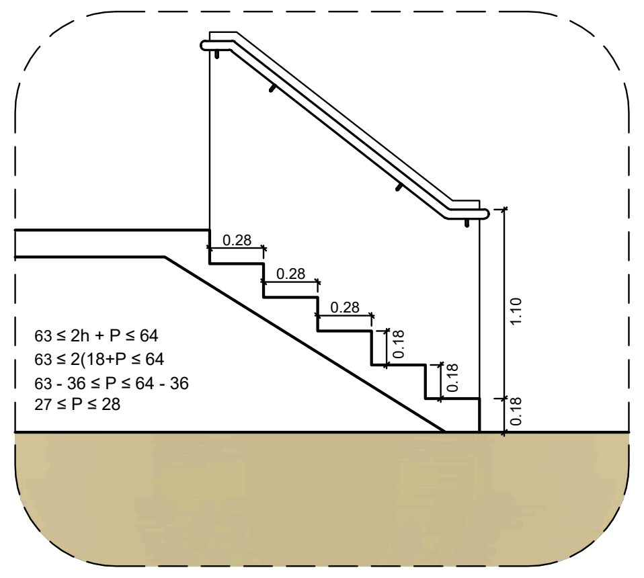

12 DET. DA ESCADA
P02 RESIDÊNCIA MULTIFAMILIAR ESC. 1/25

QUADRO DE ESQUADRIAS

ESQUADRIAS	LOCAL	DIMENSÃO (L x H)	QUANTIDADE	MATERIAL
EA01	CIRCULAÇÃO TÉRREO	2.70 x 2.10	01	ALUMÍNIO
EA02	SALAS DE ESTAR	2.60 x 2.10	05	ALUMÍNIO
EA03	SALAS DE ESTAR	2.50 x 2.10	02	ALUMÍNIO
EA04	ACESSO SOCIAL	1.20 x 2.10	01	ALUMÍNIO

ESQUADRIAS	LOCAL	DIMENSÃO (L x H)	QUANTIDADE	MATERIAL
JA01	QUARTOS/SUÍTES	1.20 x 1.10	15	ALUMÍNIO
JA02	COZINHA	1.20 x 0.50	07	ALUMÍNIO
JA03	WCS	0.50 x 1.00	09	ALUMÍNIO
JA04	WCS	0.50 x 0.50	06	ALUMÍNIO
PM01	ACESSO APTO./AP PCD	0.90 x 2.10	09	MADEIRA
PM02	QUARTOS	0.80 x 2.10	14	MADEIRA
PM03	WCS	0.70 x 2.10	14	MADEIRA
GA01	ACESSO AUTO PRINCIPAL	3.20 x 2.00	01	ALUMÍNIO
GA02	ACESSO AUTO INDIVIDUAL	2.60 x 2.00	01	ALUMÍNIO
GA03	ACESSO AUTO INDIVIDUAL	1.00 x 2.00	01	ALUMÍNIO
GA04	ACESSO LIXOS	1.50 x 2.00	01	ALUMÍNIO

OBS.: TODAS AS MEDIDAS DEVERÃO SER CONFERIDAS NA OBRA

PROPRIETÁRIO ACTIVA CONSTRUÇÕES LTDA - CNPJ: 50.056.430/0001-01
Wellington A. de Oliveira
Arquiteto e Urbanista
CAU Nº A 51775-5
PROJETO ARQ. WELLINGTON A. DE OLIVEIRA CAU Nº. A51775-5
CONSTRUÇÃO

PROJETO: CONSTRUÇÃO DE UMA EDIFICAÇÃO RESIDENCIAL MULTIFAMILIAR
LOCAL: LT-011, QD-06, DO LOTEAMENTO PORTAL DO POÇO - CABEDELO/PB
PROPRIETÁRIO: ACTIVA CONSTRUÇÕES LTDA

	ESCALA
FACHADA NORTE	1/75
FACHADA LESTE	1/75
FACHADA SUL	1/75
FACHADA OESTE	1/75
CORTES AA-BB	1/75
	1/75

E-MAIL
DATA MAIO/2026
02 / 02
PRANCHA
ÁREAS:

ENNOVE
ARQUITETURA | ENGENHARIA
ennoveprojetos@gmail.com

PREFEITURA MUNICIPAL DE CABEDELO
Secretaria do Controle do Uso e Ocupação do Solo
VISTO
ASSINADO DIGITALMENTE
Setor de Análise

PREFEITURA MUNICIPAL DE CABEDELO
Secretaria do Controle do Uso e Ocupação do Solo
APROVADO
Processo nº 382/2026
Alvará nº 2026/000147.8
ASSINADO DIGITALMENTE
Secretário

Assinado por 2 pessoas: THIAGO PAES FONSECA DANTAS e ISABELLE DOS SANTOS FIGUEIREDO
Para verificar a validade das assinaturas, acesse https://cabedelo.1doc.com.br/verificacao/8F45-F04D-7449-9EB1 e informe o código 8F45-F04D-7449-9EB1

VERIFICAÇÃO DAS ASSINATURAS

Código para verificação: 8F45-F04D-7449-9EB1

Este documento foi assinado digitalmente pelos seguintes signatários nas datas indicadas:

✓ THIAGO PAES FONSECA DANTAS (CPF 012.XXX.XXX-96) em 02/07/2026 12:27:18 GMT-03:00
Papel: Parte
Emitido por: Sub-Autoridade Certificadora 1Doc (Assinatura 1Doc)

✓ ISABELLE DOS SANTOS FIGUEIREDO (CPF 102.XXX.XXX-67) em 02/07/2026 13:09:44 GMT-03:00
Papel: Parte
Emitido por: Sub-Autoridade Certificadora 1Doc (Assinatura 1Doc)

Para verificar a validade das assinaturas, acesse a Central de Verificação por meio do link:

https://cabedelo.1doc.com.br/verificacao/8F45-F04D-7449-9EB1